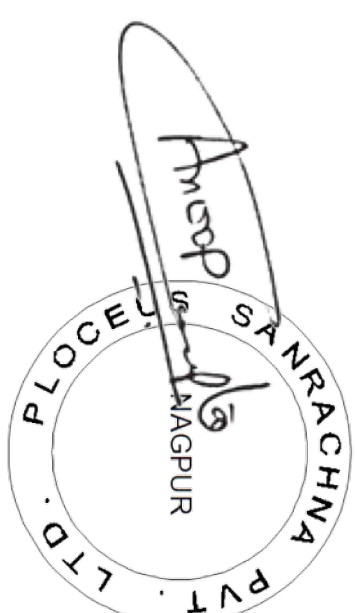
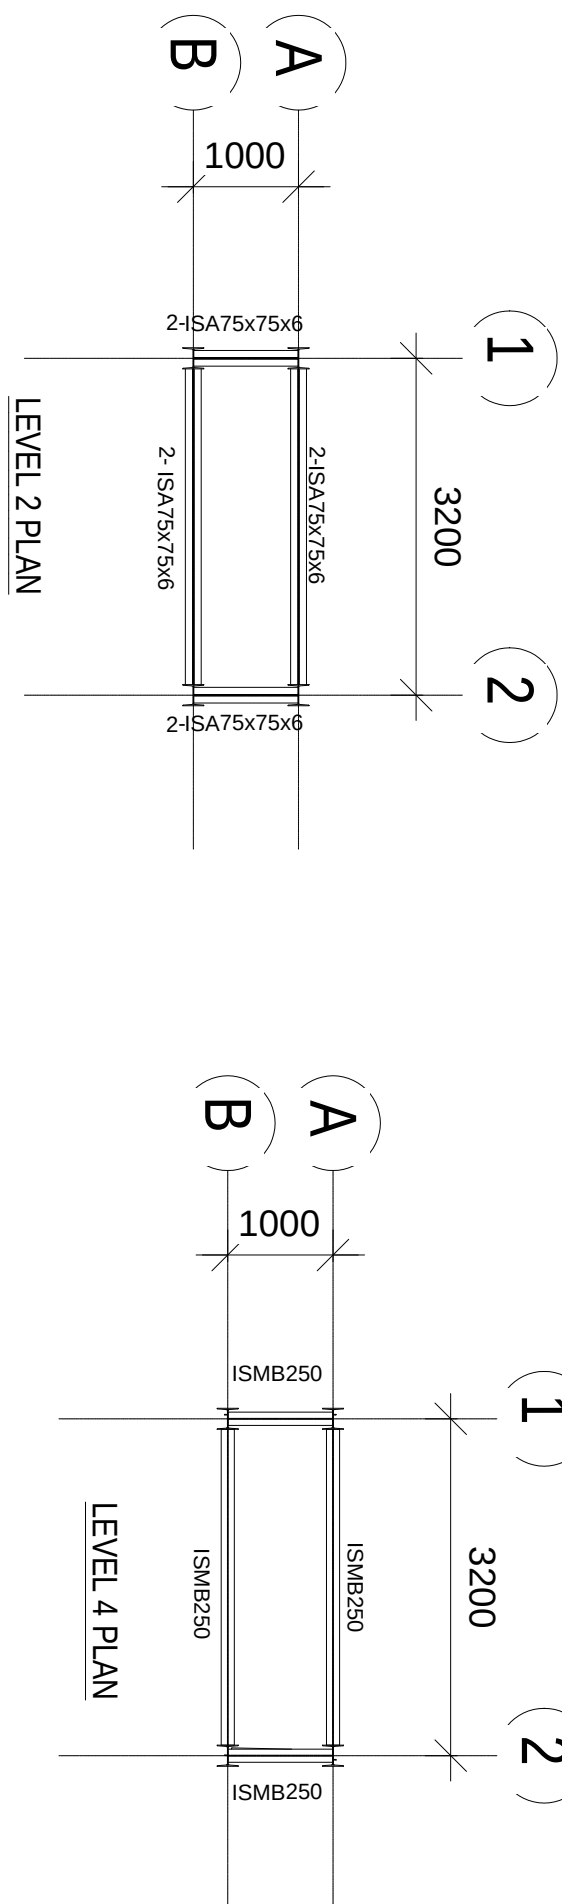
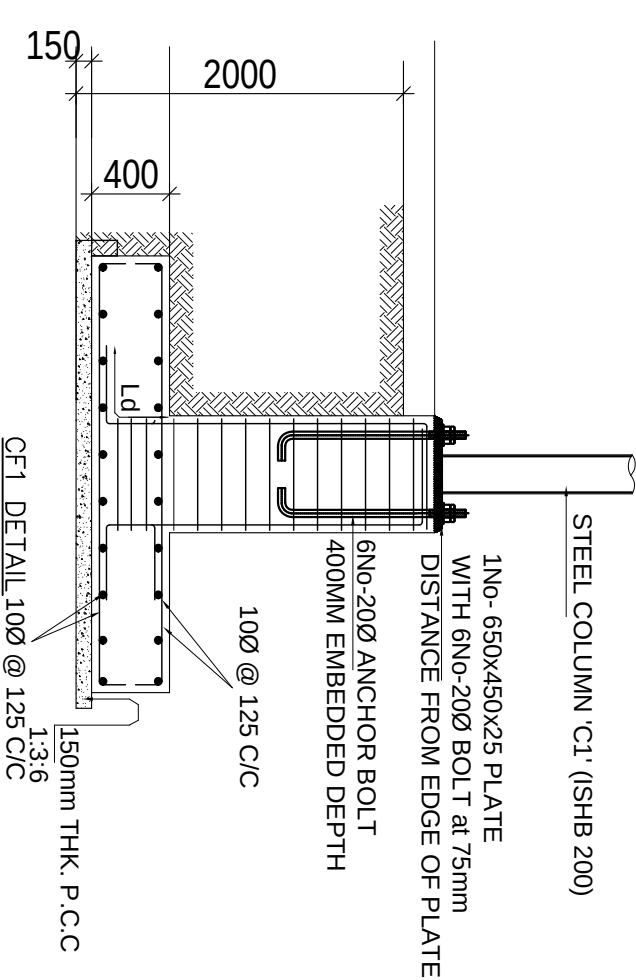
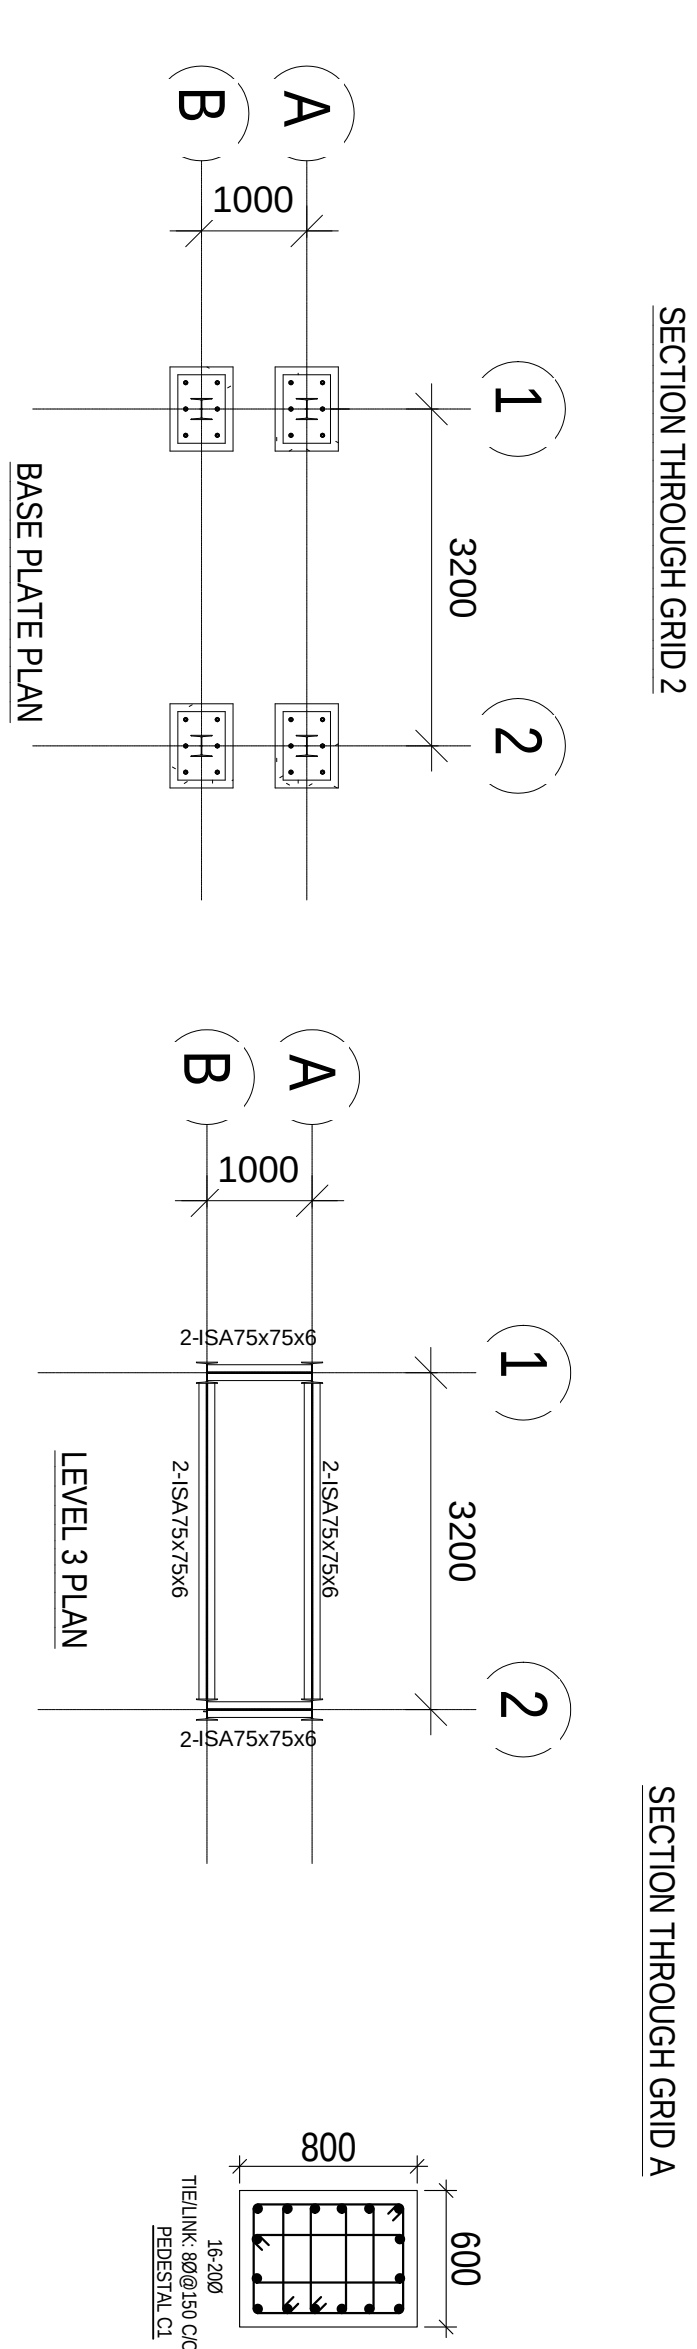
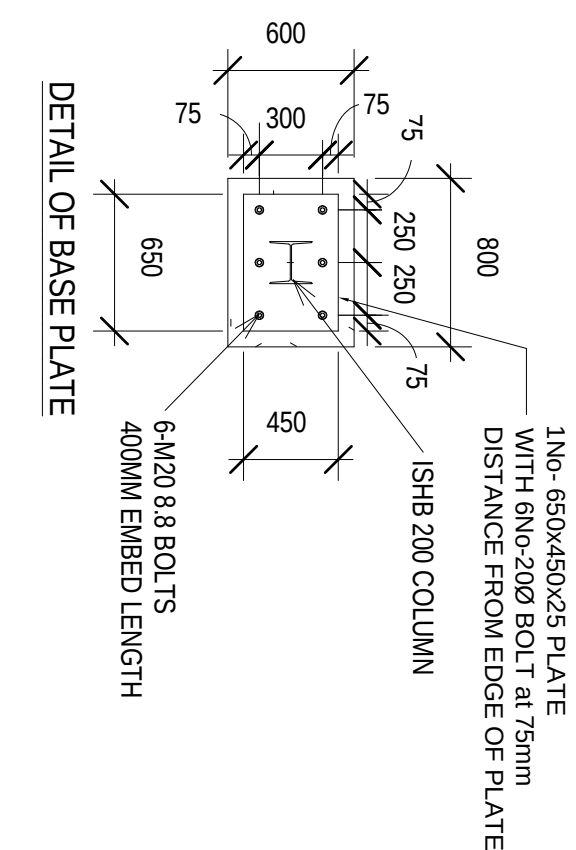
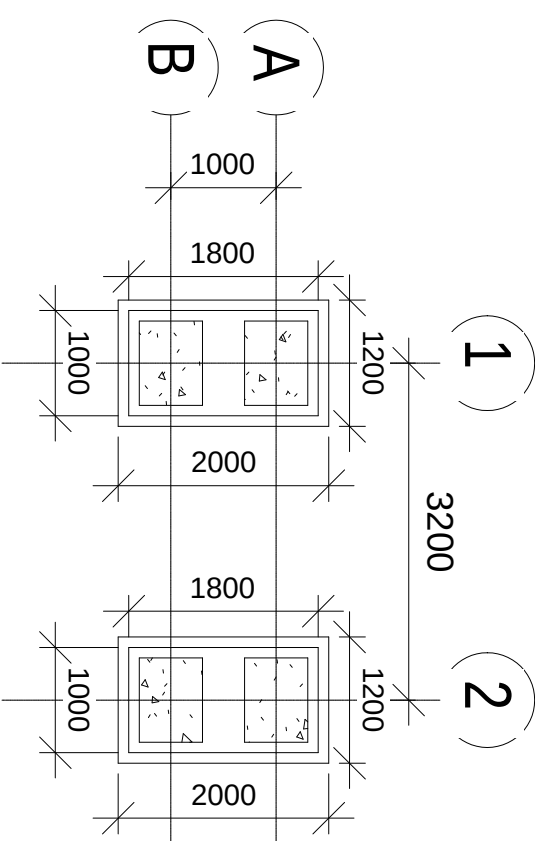
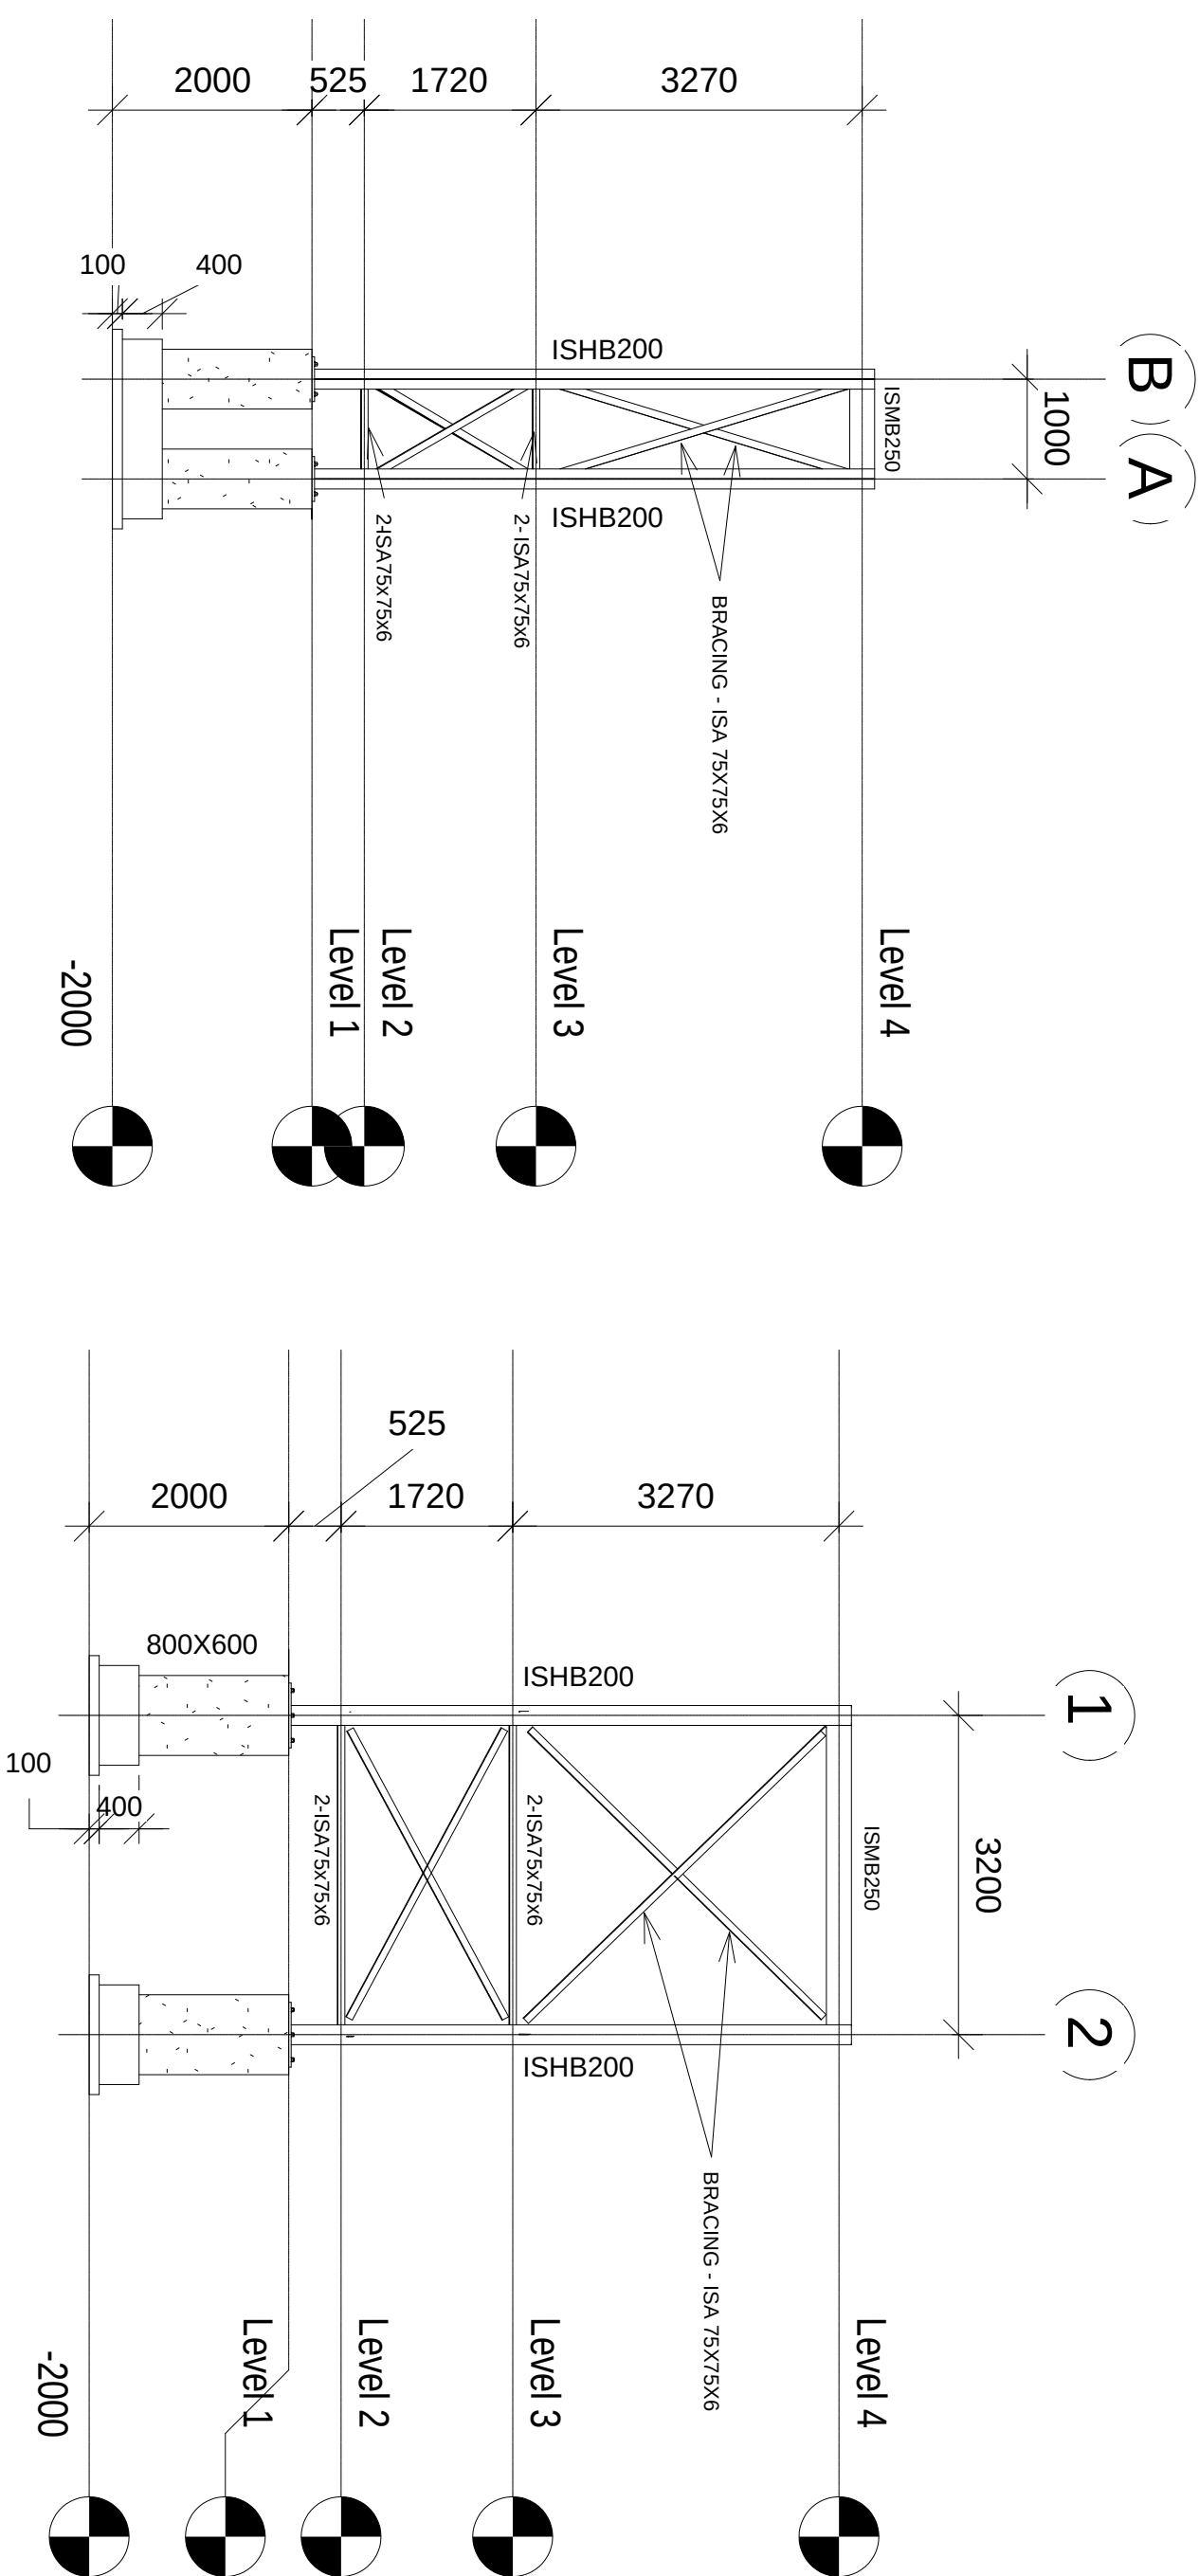


[illegible][illegible]

CLIENT :  Indian Railways

CONTRACTOR :  **ZETWERK**
 MACHINE PRODUCTIEN
 M/S ZIMBEL-VFC (JV)

 **YFC**
 PROJECTS

PROJECT : MAJOR UPGRADE OF KOTA RAILWAY STATION OF ENGINEERING PROCUREMENT AND CONSTRUCTION (EPC) MODE

CONSULTANT:

MASTERPLANNING | ARCHITECTURE | DESIGN

o/a

DESIGN FORUM
OF ARCHITECTS

Advant IT Park Tower-B, Unit-602
Sector-142 Expressway Noida-201301.
TEL:0120-4601000 EMAIL: info@dfam

STRUCTURAL DESIGN SECTION					STRUCTURE/RECORD:
PROJECT: 04000000000000000000 JOB: 04000000000000000000 DRAWING NO.: 04000000000000000000		REVISIONS: 04000000000000000000 DATE: 04000000000000000000			
STAGE:	DESIGN	APPROVED BY:	CHECKED BY:		
DERIVATIVE	ds	DATE:	dk		
	SCALE: 1/4" = 1'-0"	DATE OF ISSUE:			
	1:160	21.09.2026			
Structural details of Escalator					
CATEGORY:			STR		
DRAWING TITLE			REF. NO.:		
20040-STR-ES-ESCALATOR-S1			RO		