

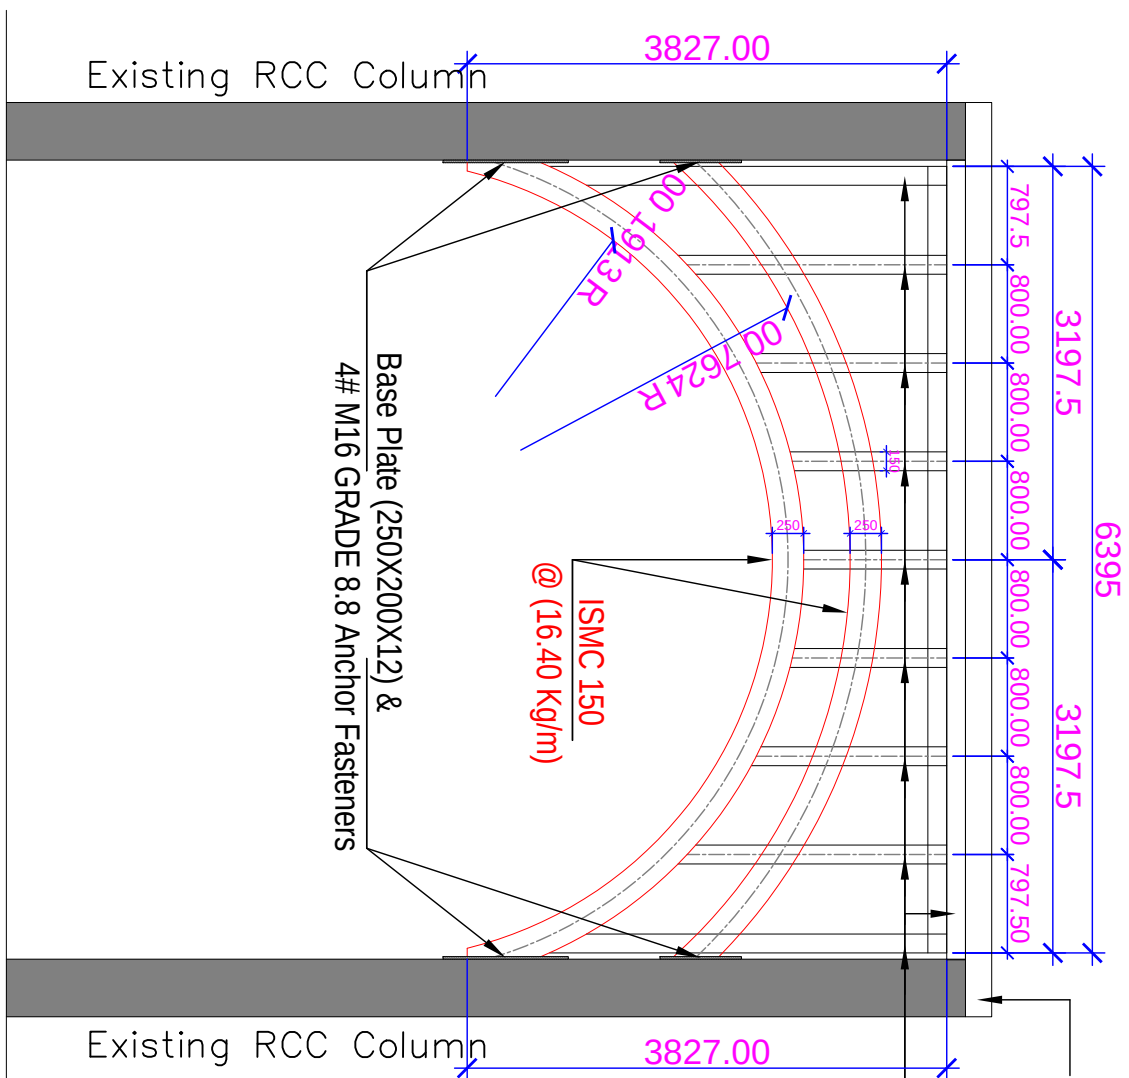
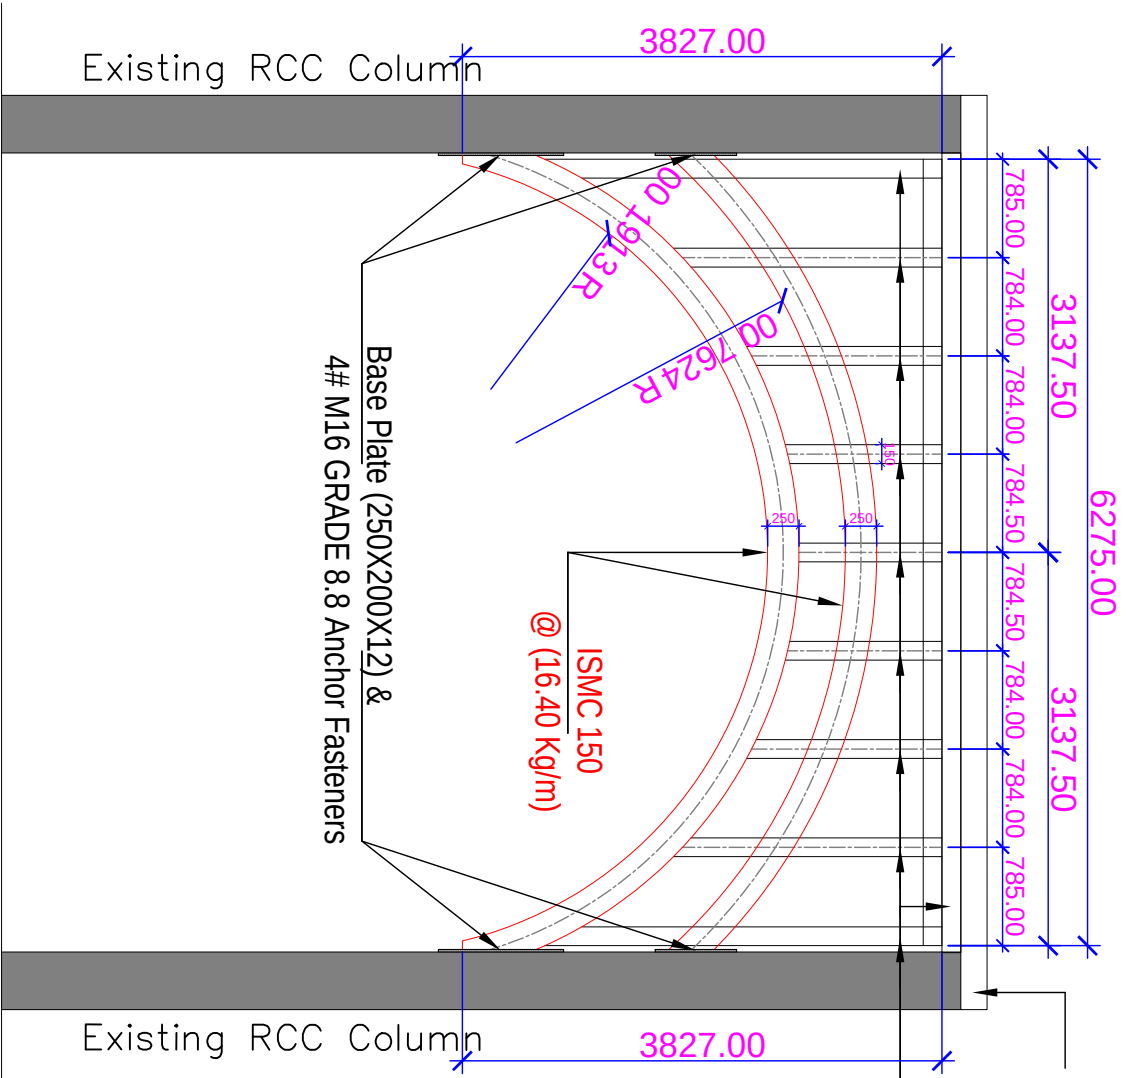
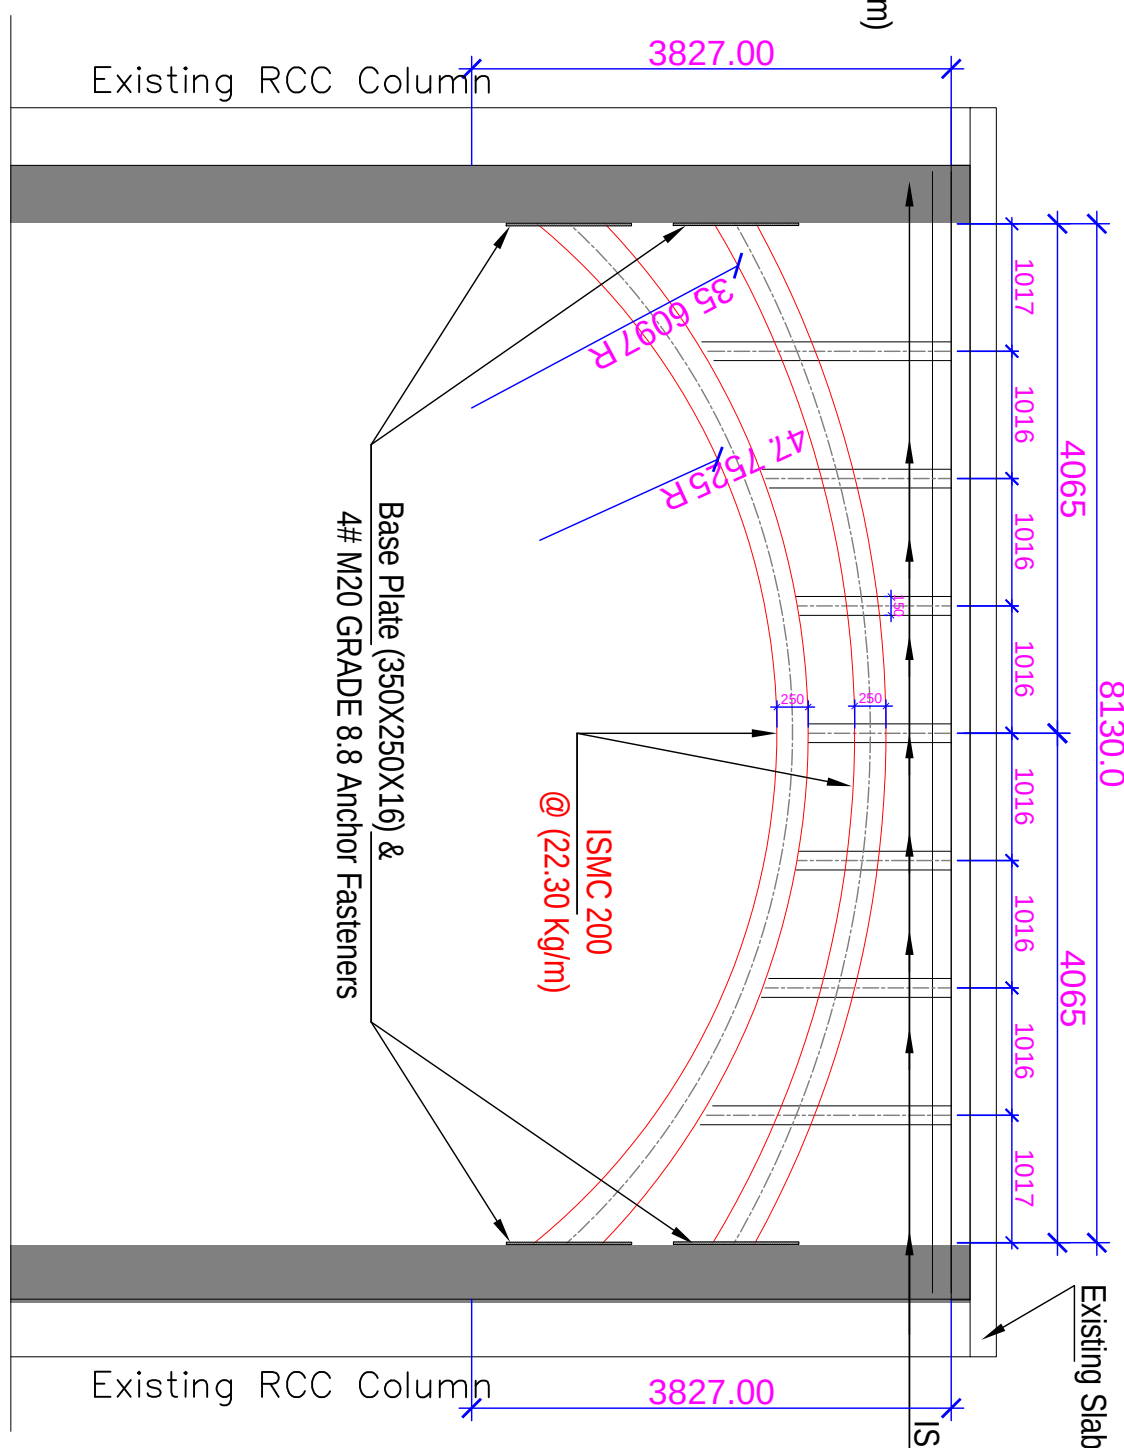


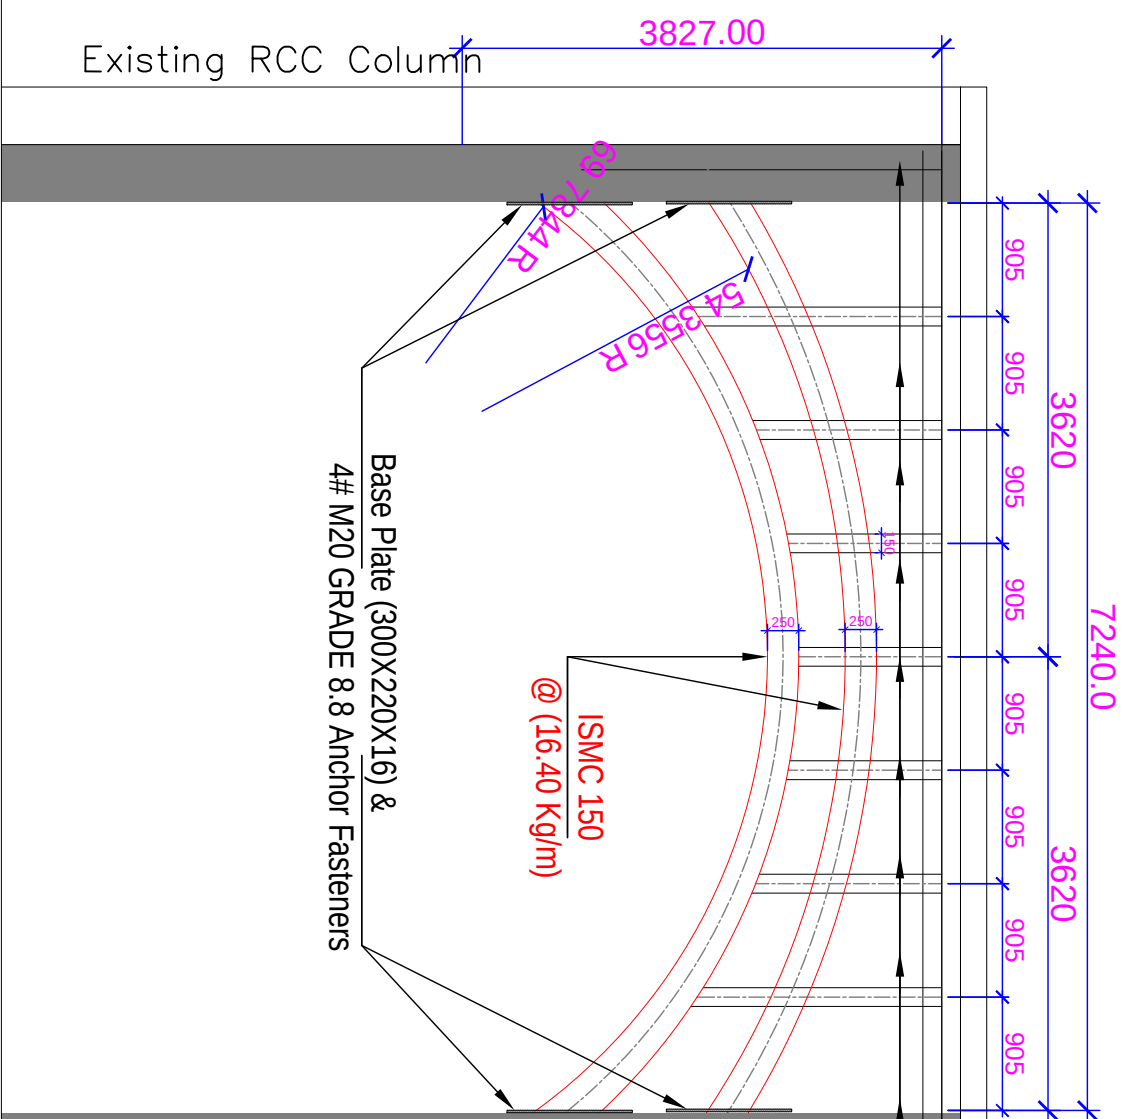

150 Kg/m)				SUMMARY OF COMBINED TABLE FOR (ISMIC TO SIDE COLUMNS) CONNECTIONS		
Component / Design Parameter	Element 1 (6-275m Span) FDP	Element 2 (7-240m Span) FDP	Element 3 (8-130m Span) FDP			
Main Facade Section	ISMIC 150	ISMIC 150	ISMIC 200			
Base Plate Size	250 × 200 × 12 mm	300 × 220 × 16 mm	350 × 250 × 16 mm			
Gusset Plates per Base Plate	2 Nos.	2 Nos.	4 Nos.			
Gusset Plate Dimensions	100 × 100 × 8 mm	120 × 120 × 10 mm	150 × 120 × 10 mm			
Chemical Anchor Bolts	4 Nos. M16 (Grade 8.8)	4 Nos. M20 (Grade 8.8)	4 Nos. M20 (Grade 8.8)			
Min. Bolt Embedment Depth	125 mm	160 mm	160 mm			
Shop Fillet Weld Size	6 mm Continuous	6 mm Continuous	8 mm Continuous			
Bolt Interaction Ratio	0.413 (≤ 1.0)	0.085 (≤ 1.0)	0.459 (≤ 1.0)			
Connection Safety Status	STRUCTURALLY SAFE	STRUCTURALLY SAFE	STRUCTURAL			

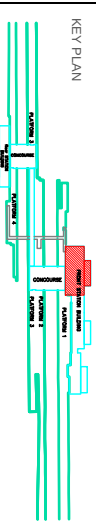

SUMMARY OF (ISMCC TO TOP SLAB) CONNECTIONS			
Design Parameter	Element 1 (6x275mm Span) PDF	Element 2 (7x240mm Span) PDF	Element 3 (8x130mm Span) PDF
Facade Section	ISMCC 160	ISMCC 160	ISMCC 200
Factored Downward Tension (T_{ult})	15.53 kN	20.53 kN	26.13 kN
Factored Wind Shear (V_{ult})	8.57 kN	11.39 kN	14.36 kN
Top Plate Size	200 x 150 x 10 mm	220 x 160 x 12 mm	250 x 180 x 12 mm
Plate Bending Utilization	75.5%	79.9%	86.1%
Chemical Anchor Bolts	2 Nos. M16 (Grade 8.8)	2 Nos. M16 (Grade 8.8)	2 Nos. M20 (Grade 8.8)
Mfr. Bolt Embedment	125 mm	125 mm	160 mm
Combined Bolt Interaction Ratio	0.0935 (≤ 1.0)	0.0660 (≤ 1.0)	0.0938 (≤ 1.0)
Overall Safety Status	STRUCTURALLY SAFE	STRUCTURALLY SAFE	STRUCTURALLY SAFE

[illegible]

The image shows the cover page of a tender document. On the left, there is a large, stylized 'ofa' logo in a light gray font. In the center, there is a photograph of the Kota Railway Station, showing its modern architecture with a large, curved roof and multiple levels. To the right of the photograph, there is a vertical sidebar containing several elements: at the top, the text 'West Central Railway' in a bold, black font; below it, the logo of the West Central Railway, which is a circular emblem with a train and the text 'WEST CENTRAL RAILWAY' and 'भारतीय रेलवे' (Indian Railways); further down, the logos for 'ZETWERK' (with the tagline 'MULTISPECIALISING') and 'YFPC PROJECTS' (with a stylized 'Y' logo); and at the bottom, the text 'M/S ZINPRE - YFPC (P)' in a bold, black font. The top of the page has the text 'CONSULTANT' in a bold, black font. The right side of the page has the text 'PROJECT' in a bold, black font, followed by the title 'UPGRADATION OF KOTA RAILWAY STATION OF ENGINEERING PROCUREMENT AND CONSTRUCTION (EPC) MODE' in a bold, black font. The bottom of the page has the text 'CONSULTANT' in a bold, black font, followed by the text 'MASTERPLANNING | ARCHITECTURE | DESIGN' in a bold, black font.

DWG NO	DRAWING TITLE	STAGE :	DESIGN DERIVATIVE	DATE OF CONSTRUCTION	DATE OF REVISION	APPROVED BY :  RAVI GARG	PROJECT NO.	PROJECT NAME
2004D-AR-FAL-FACADE-S1	Structural details of Facade	DRAWN BY :	d.s	22.05.2024				
REV / NO	CATEGORY :	REVIEWED BY :	dk					
RO	ARCH	NORTH						